
MKSPEC · КАРТА СЕТИ

Карта сети — 1 этаж (Козина 7, пом. 1080 + 1079)

г. Казань, ул. Алексея Козина, д. 7 · помещения 1080 + 1079 · 1 этаж

Масштаб 1:100 · h = 3.96 м
Площадь: 396 м² · стен: 63
03.11.2026 · лист 1 из 1
Михаил · администратор

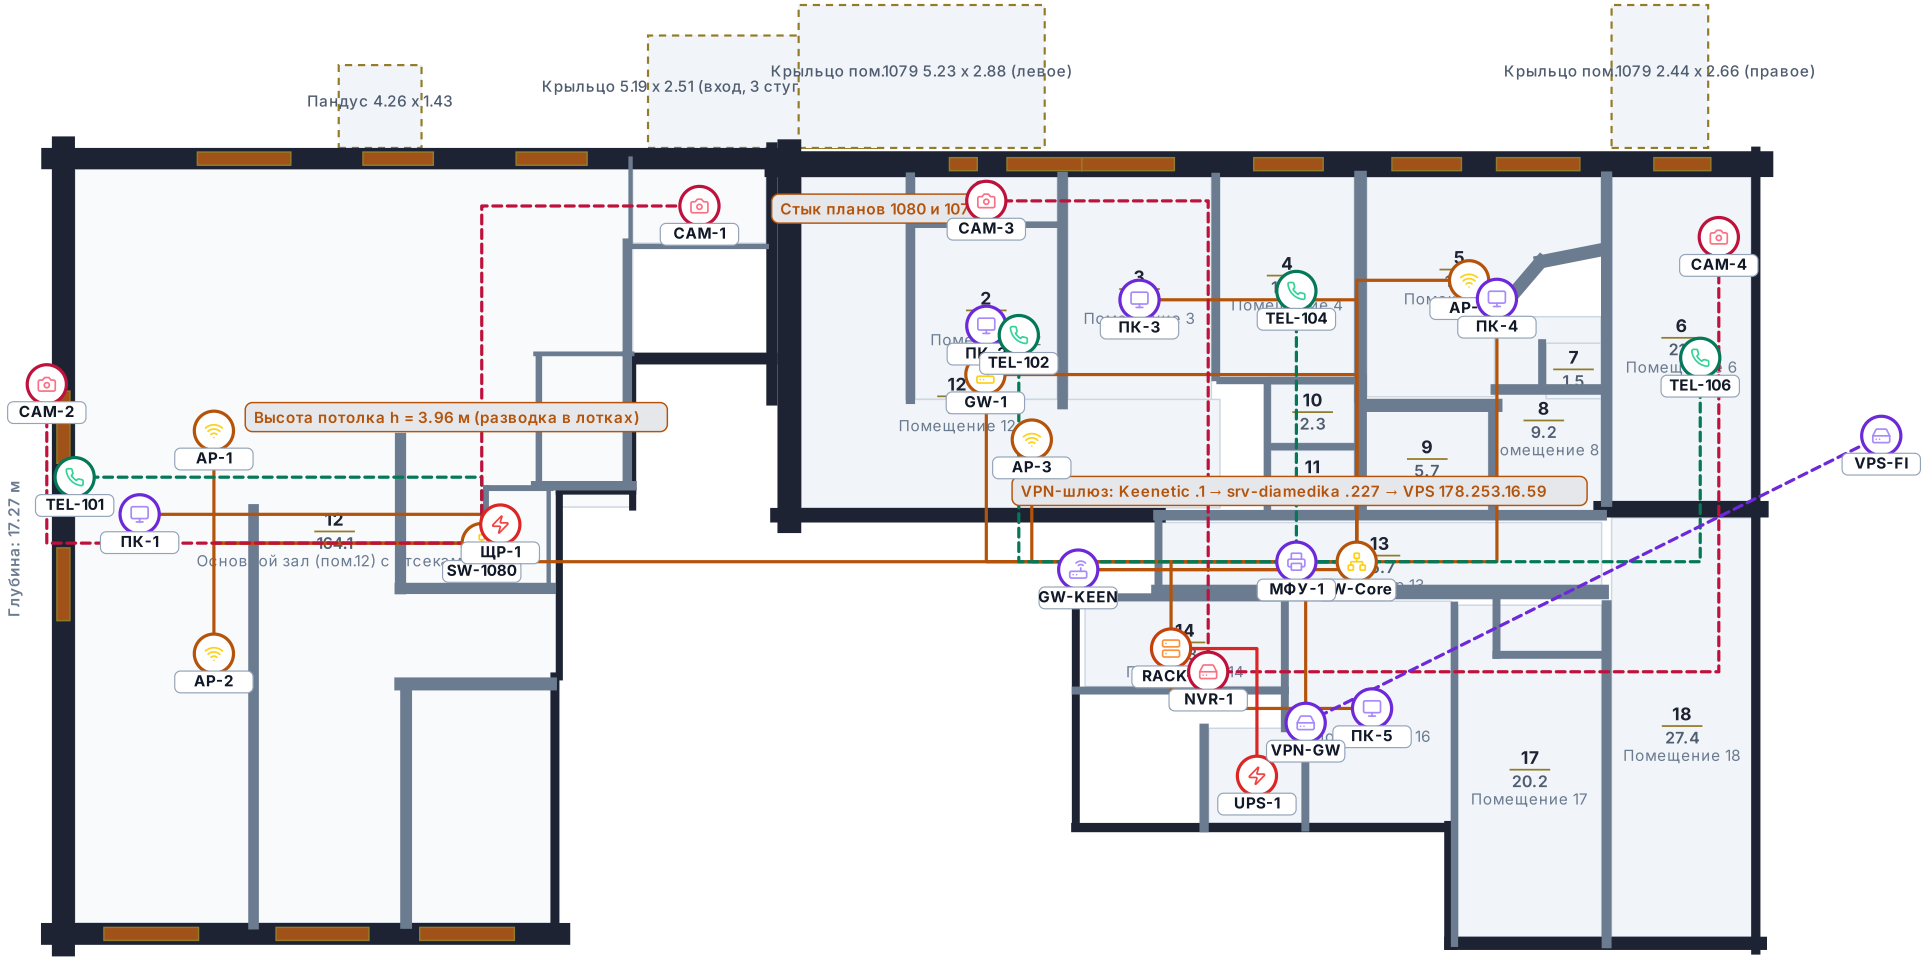

Интернет / СКС · Телефония (SIP) · ПК и рабочие места · Серверы и ядро сети · Видеонаблюдение · Электрика и питание 220В · Перегородки (редакт.) · Пометки и размеры · VPN / шлюз

UTP Cat.6: 198.1 м (14) · Оптика OM4: 40.5 м (2) · UTP Cat.5e (Tel): 71.1 м (4) · UTP Cat.6 PoE: 81.1 м (4) · ВВГнг 3x2.5: 19.5 м (2) · VPN tunnel: 22.6 м (1)

Схема сети: узлов 28, кабельных трасс 27, суммарный метраж 432.9 м. Слой «VPN / шлюз» — логические объекты документации.